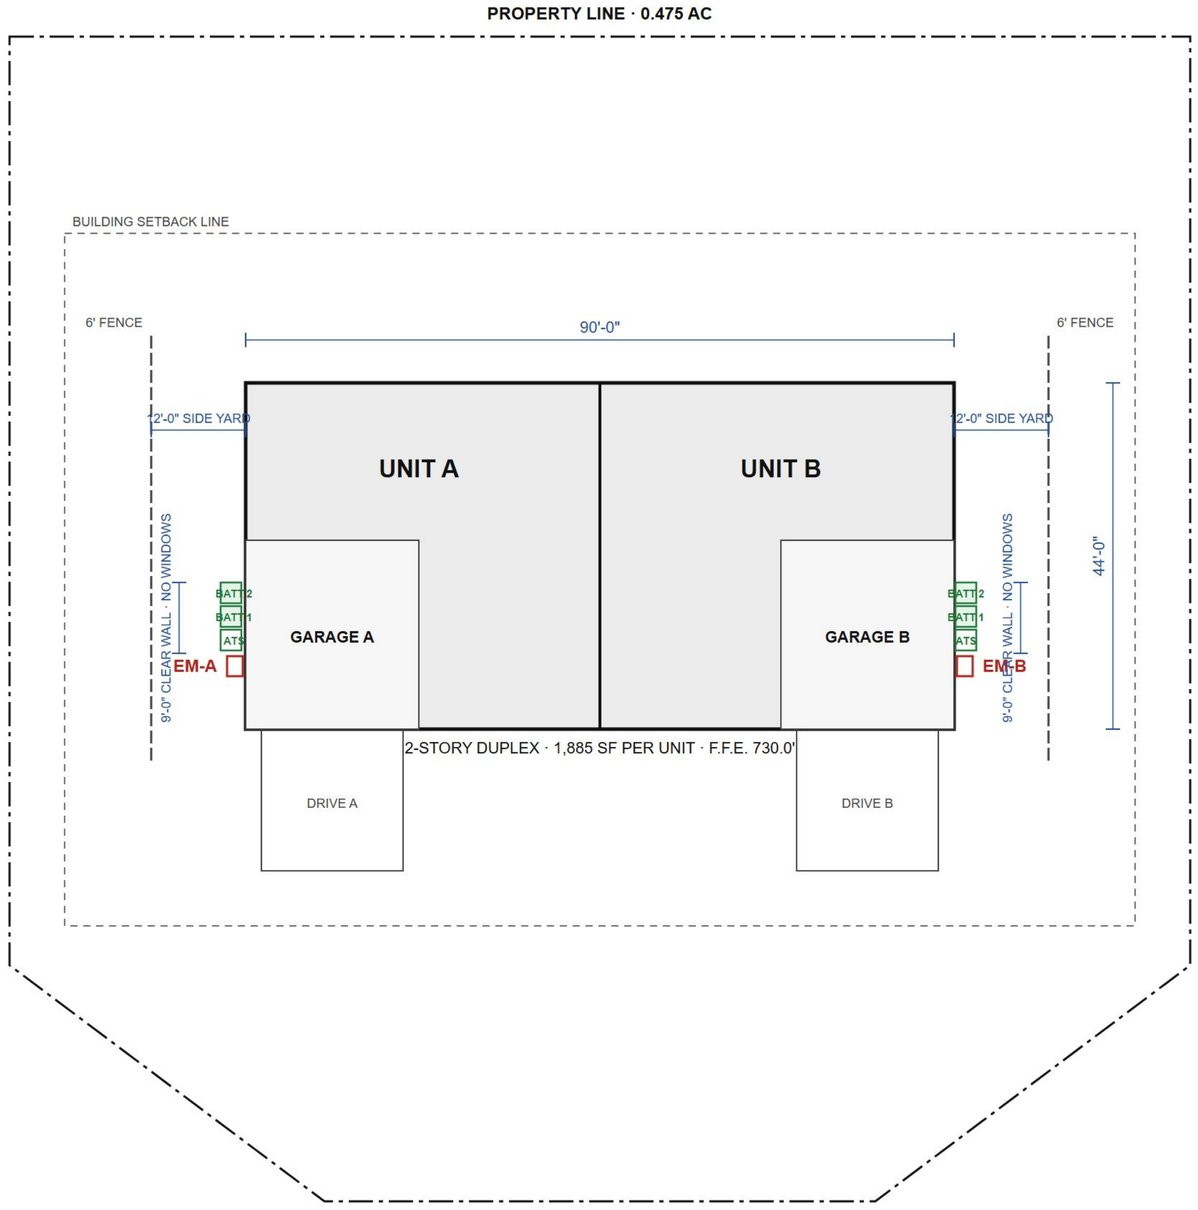


N

SITE NOTES:

1. ALL-ELECTRIC UNITS · NO GAS SERVICE OR GAS METER ON SITE.
2. ELECTRIC METERS EM-A / EM-B ON OUTER GARAGE SIDE WALLS, 5'-0" A.F.F. TO CENTER.
3. BATTERY ZONE: 9'-0" CLEAR EXTERIOR WALL FROM METER (30" ATS + TWO 3'x3' PADS), PADS WITHIN 1'-0" OF WALL, WITHIN 20'-0" OF METER. NO TRENCHING REQUIRED.
4. BATTERY ZONE KEEP CLEAR: NO LANDSCAPING, A/C, HOSE BIBS OR FENCE POSTS.
5. PAD AREA FINISH-GRADED LEVEL (±1%). FEMA ZONE X.
6. SIDE YARD 12'-0" WALL TO FENCE (≥ 56" REQUIRED: BATTERY + 32-38" WALKWAY).
7. NO PHOTOVOLTAIC SYSTEM IN THIS SCOPE.

SAMPLE PLAN SET
FOR DEMONSTRATION ONLY

PROJECT
DUPLEX RESIDENCE · UNITS A & B

ADDRESS
104 GUNNER RD

BUDA, TX 78610

LEGAL
LOT 20, BLOCK D

EMMA PARK SUBD. PH. 2

COUNTY
HAYS · PROP ID 205025

UTILITY
PEDERNALES ELEC. COOP

SERVICE
200A PER UNIT · 120/240V

DATE
2025 PERMIT SET (SAMPLE)


SCALE
1" = 10'-0"

SHEET NAME
SITE / PLOT PLAN

A1.0

NOT FOR CONSTRUCTION

PARTIAL PLAN · UNIT A GARAGE / METER WALL (UNIT B MIRROR)

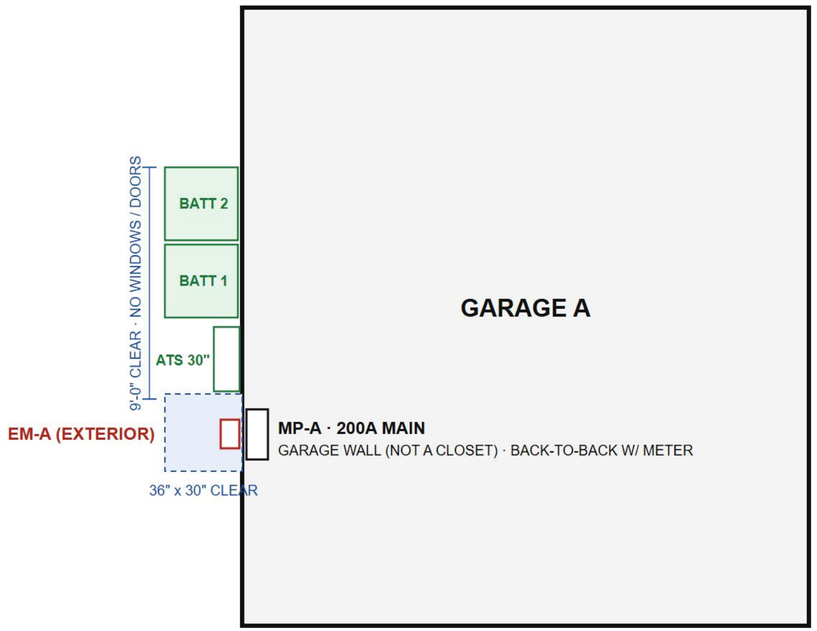

ELECTRICAL RISER DIAGRAM (PER UNIT)

PEC UTILITY
UNDERGROUND SERVICE LATERAL

↓

METER SOCKET
CL200 · 200A · EM-A

↓

MAIN PANEL MP-A
200A MAIN BREAKER · 200A BUS · 40 CKT

ONE (1) MAIN PANEL PER DWELLING UNIT
NO SUBPANELS · NO PV · NO GENERATOR

SERVICE & LOAD SUMMARY · UNIT A (UNIT B IDENTICAL)

SERVICE SIZE	200A, 120/240V, 1Ø, 3W
MAIN BREAKER	200A
CALCULATED LOAD (NEC 220.82)	118A
HVAC	3-TON HEAT PUMP (ALL-ELECTRIC)
WATER HEATER	50 GAL ELECTRIC
RANGE / DRYER	ELECTRIC
METER HEIGHT	5'-0" A.F.F. TO CENTER

ELECTRICAL NOTES:

1. METER AND MAIN PANEL SHARE THE SAME EXTERIOR WALL (BACK-TO-BACK).
2. PROVIDE 30" CLEAR WALL ADJACENT TO METER FOR BATTERY TRANSFER SWITCH.
3. MAINTAIN NEC 110.26 WORKING SPACE 36" DEEP x 30" WIDE AT METER AND PANEL.
4. HARNESS ROUTED SURFACE ON WALL · NO TRENCHING OR ATTIC RUNS.

SAMPLE PLAN SET
FOR DEMONSTRATION ONLY

PROJECT
DUPLEX RESIDENCE · UNITS A & B

ADDRESS
104 GUNNER RD

BUDA, TX 78610

LEGAL
LOT 20, BLOCK D

EMMA PARK SUBD. PH. 2

COUNTY
HAYS · PROP ID 205025

UTILITY
PEDERNALES ELEC. COOP

SERVICE
200A PER UNIT · 120/240V

DATE
2025 PERMIT SET (SAMPLE)


SCALE
1/4" = 1'-0"

SHEET NAME
ELECTRICAL PLAN & RISER

E1.0

NOT FOR CONSTRUCTION

WEST ELEVATION · UNIT A GARAGE SIDE WALL (METER WALL) · UNIT B EAST ELEVATION MIRROR

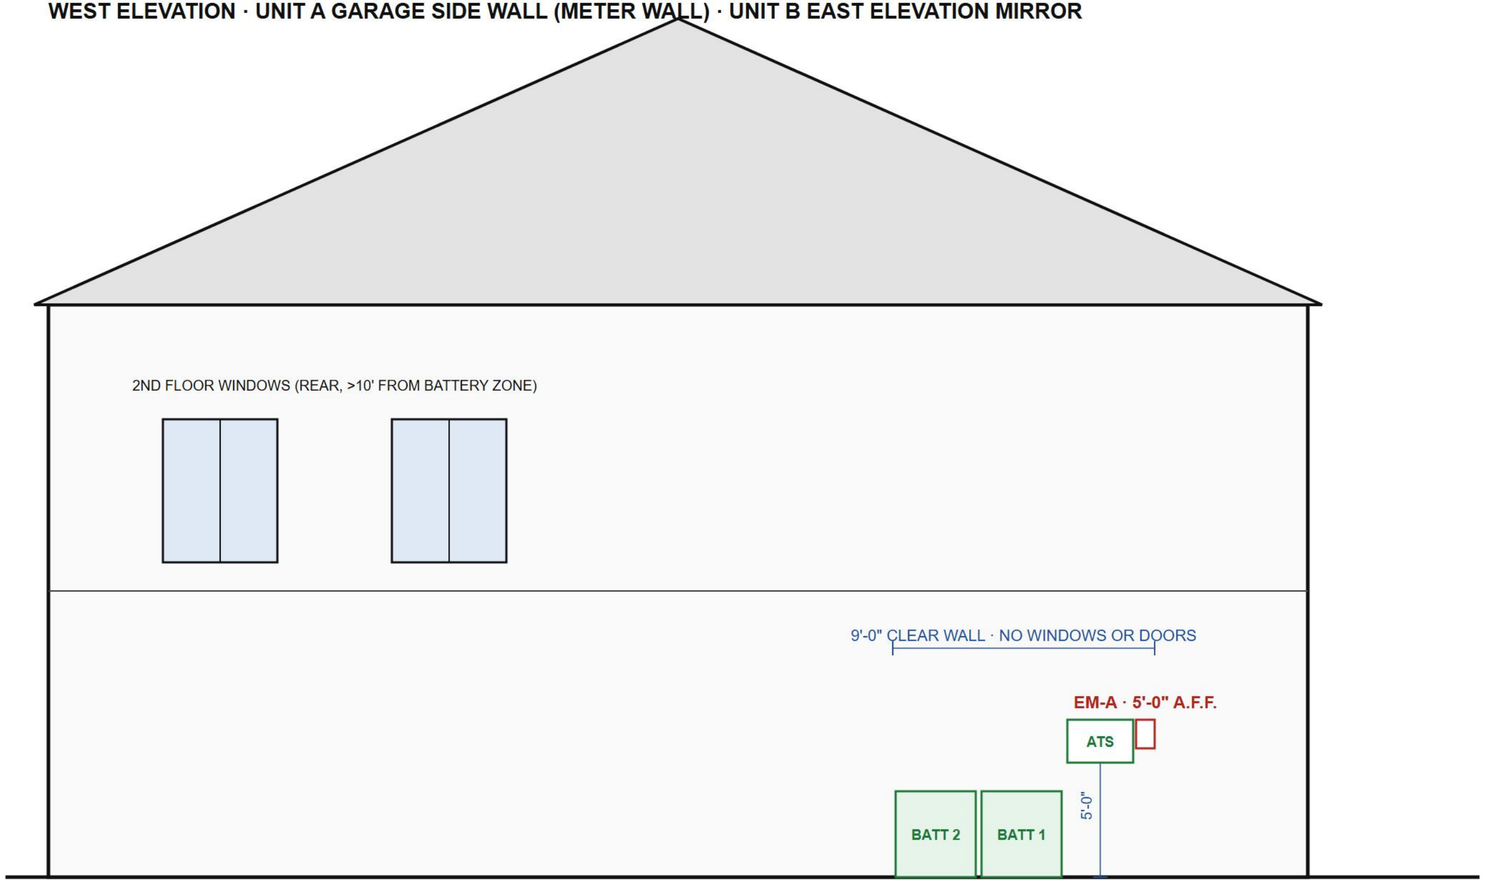

FINISH GRADE · LEVEL AT BATTERY PADS (±1%)

SAMPLE PLAN SET
FOR DEMONSTRATION ONLY

PROJECT
DUPLEX RESIDENCE · UNITS A & B

ADDRESS
104 GUNNER RD

BUDA, TX 78610

LEGAL
LOT 20, BLOCK D

EMMA PARK SUBD. PH. 2

COUNTY
HAYS · PROP ID 205025

UTILITY
PEDERNALES ELEC. COOP

SERVICE
200A PER UNIT · 120/240V

DATE
2025 PERMIT SET (SAMPLE)

SCALE
1/4" = 1'-0"

SHEET NAME
EXTERIOR ELEVATIONS

A3.0

NOT FOR CONSTRUCTION