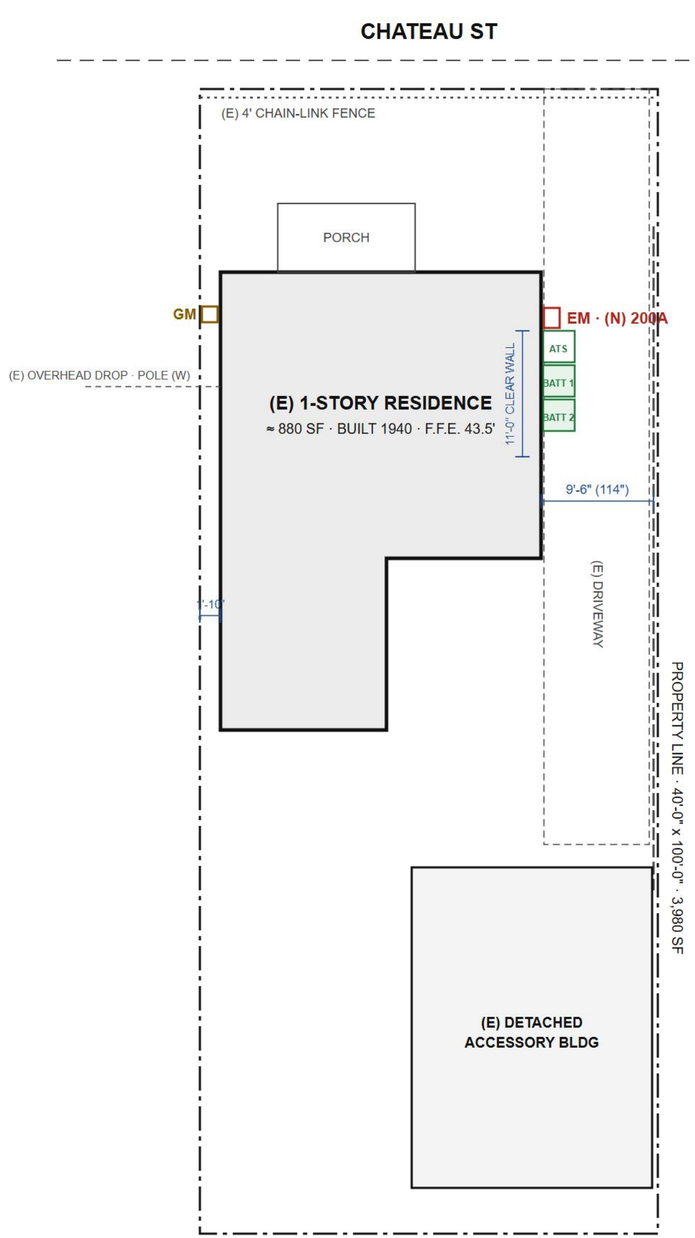


N

SITE NOTES:

1. (N) 200A OVERHEAD SERVICE; METER EM RELOCATED TO EAST WALL, 5'-0" A.F.F. TO CENTER.
2. (E) GAS METER GM ON WEST WALL · OPPOSITE SIDE OF HOUSE FROM BATTERY ZONE (>30' AWAY).
3. BATTERY ZONE: 11'-0" CLEAR EAST WALL FROM METER (30" ATS + TWO 3'x3' PADS), NO WINDOWS.
4. PADS WITHIN 1'-0" OF WALL AND 20'-0" OF METER · HARNESS SURFACE-RUN · NO TRENCHING.
5. EAST SIDE YARD 9'-6" (114") WALL TO FENCE (≥ 56" REQ'D) · WEST SIDE YARD 1'-10" NOT USED.
6. BATTERY ZONE KEPT CLEAR OF A/C, HOSE BIBS AND LANDSCAPING · GRADE LEVEL ±1% · FEMA ZONE X.
7. NO PHOTOVOLTAIC SYSTEM IN THIS SCOPE.

ARCHITECTURAL DRAWINGS

PROJECT
SINGLE-FAMILY RESIDENCE

RENOVATION · SERVICE UPGRADE

ADDRESS
8014 CHATEAU ST

HOUSTON, TX 77028

COUNTY
HARRIS · HCAD 0300170170004

USE / YEAR
A1 SINGLE-FAMILY · BUILT 1940

UTILITY
CENTERPOINT ENERGY

SERVICE
(N) 200A · 120/240V · OVERHEAD

SET
ARCH · A1.0 / E1.0 / A3.0 / A4.0


SCALE
1" = 8'-0"

SHEET NAME
SITE / PLOT PLAN

A1.0

ILLUSTRATIVE SAMPLE
NOT FOR CONSTRUCTION

PARTIAL PLAN · EAST WALL AT UTILITY ROOM / METER

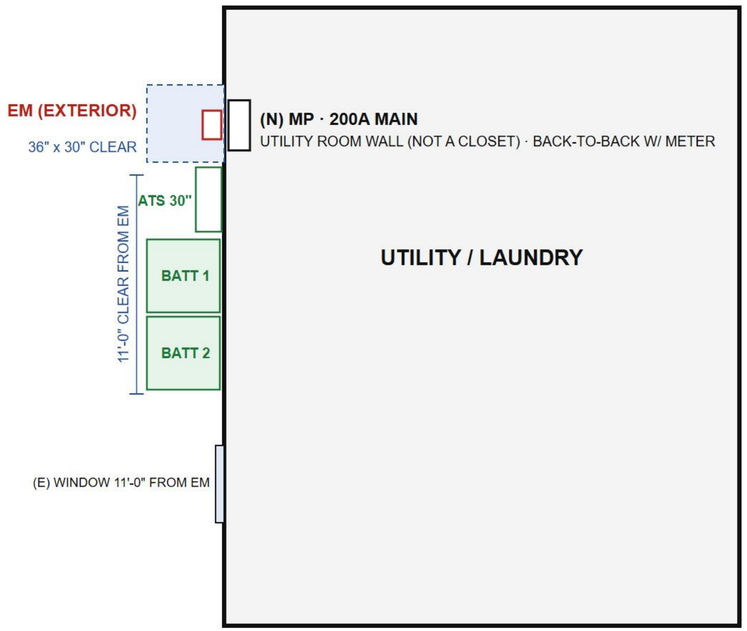

ELECTRICAL RISER DIAGRAM

CENTERPOINT ENERGY
(E) OVERHEAD SERVICE DROP · (N) MAST + WEATHERHEAD

↓

METER SOCKET
(N) CL200 · 200A · EAST WALL

↓

MAIN PANEL MP
(N) 200A MAIN BREAKER · 200A BUS · 30 CKT

ONE (1) MAIN PANEL · (E) 100A FUSE PANEL REMOVED
NO SUBPANELS · NO PV · NO GENERATOR

SERVICE & LOAD SUMMARY

SERVICE SIZE	(N) 200A, 120/240V, 1Ø, 3W
MAIN BREAKER	200A
CALCULATED LOAD (NEC 220.82)	84A
HVAC	(N) 2-TON HEAT PUMP
WATER HEATER	(E) 40 GAL GAS
RANGE / DRYER	ELECTRIC / GAS
METER HEIGHT	5'-0" A.F.F. TO CENTER

ELECTRICAL NOTES:

1. METER AND MAIN PANEL SHARE THE EAST EXTERIOR WALL (BACK-TO-BACK).
2. PROVIDE 30" CLEAR WALL ADJACENT TO METER FOR BATTERY TRANSFER SWITCH.
3. MAINTAIN NEC 110.26 WORKING SPACE 36" DEEP x 30" WIDE AT METER AND PANEL.
4. PANEL NOT IN A CLOTHES CLOSET (NEC 240.24(D)) · METER + MAST SECURELY ATTACHED (NEC 110.12).
5. HARNESS ROUTED SURFACE ON WALL · NO TRENCHING OR ATTIC RUNS.

ARCHITECTURAL DRAWINGS

PROJECT
SINGLE-FAMILY RESIDENCE

RENOVATION · SERVICE UPGRADE

ADDRESS
8014 CHATEAU ST

HOUSTON, TX 77028

COUNTY
HARRIS · HCAD 0300170170004

USE / YEAR
A1 SINGLE-FAMILY · BUILT 1940

UTILITY
CENTERPOINT ENERGY

SERVICE
(N) 200A · 120/240V · OVERHEAD

SET
ARCH · A1.0 / E1.0 / A3.0 / A4.0


SCALE
1/4" = 1'-0"

SHEET NAME
ELECTRICAL PLAN & RISER

E1.0

ILLUSTRATIVE SAMPLE
NOT FOR CONSTRUCTION

EAST ELEVATION · METER WALL (DRIVEWAY SIDE)

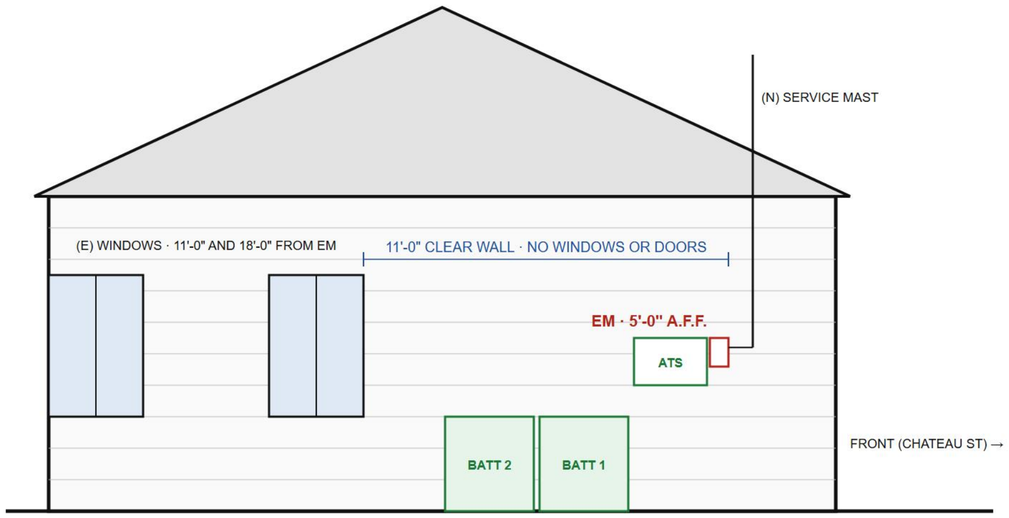

FINISH GRADE · LEVEL AT BATTERY PADS (±1%)

ARCHITECTURAL DRAWINGS

PROJECT
SINGLE-FAMILY RESIDENCE

RENOVATION · SERVICE UPGRADE

ADDRESS
8014 CHATEAU ST

HOUSTON, TX 77028

COUNTY
HARRIS · HCAD 0300170170004

USE / YEAR
A1 SINGLE-FAMILY · BUILT 1940

UTILITY
CENTERPOINT ENERGY

SERVICE
(N) 200A · 120/240V · OVERHEAD

SET
ARCH · A1.0 / E1.0 / A3.0 / A4.0

SCALE
1/4" = 1'-0"

SHEET NAME
EXTERIOR ELEVATION

A3.0

ILLUSTRATIVE SAMPLE
NOT FOR CONSTRUCTION

BASE POWER UNIT · INSTALL REQUIREMENT COMPLIANCE SCHEDULE

This schedule states the as-designed value for each requirement, cross-referenced to the sheet and note that governs it.

#	REQUIREMENT	AS-DESIGNED VALUE	STATUS	REFERENCE
C1	PANEL SIZE	1 (N) MAIN PANEL · 200A MAIN BREAKER · 200A BUS (E) 100A FUSE PANEL REMOVED	COMPLIES	E1.0 RISER DIAGRAM · SERVICE & LOAD SUMMARY
C2	METER & PANEL LOCATION	METER (EM) & MAIN PANEL (MP) BACK-TO-BACK ON EAST EXTERIOR WALL · EM 5'-0" A.F.F.	COMPLIES	E1.0 PARTIAL PLAN, NOTE 1 · A3.0 ELEVATION
C3	WALL SPACE AT METER	11'-0" CLEAR EAST WALL FROM EM · NO WINDOWS OR DOORS (NEAREST WINDOW 11'-0")	COMPLIES	A1.0 NOTE 3 · A3.0 ELEVATION
C4	SIDE CLEARANCE	EAST SIDE YARD 9'-6" (114") WALL-TO-FENCE ≥ 56" MIN. REQUIRED	COMPLIES	A1.0 SITE PLAN, NOTE 5
C5	GAS METER SEPARATION	GAS METER (GM) ON WEST WALL, OPPOSITE SIDE OF HOUSE, > 30'-0" FROM BATTERY ZONE ≥ 3'-0" MIN. REQUIRED	COMPLIES	A1.0 NOTE 2
C6	NEC WORKING SPACE	36" DEEP x 30" WIDE CLEAR AT EM & MP (110.26) · MP NOT IN CLOSET (240.24(D)) · EM/MAST SECURE (110.12)	COMPLIES	E1.0 NOTE 2-4

RESULT

ALL 6 REQUIREMENTS COMPLY · SITE ELIGIBLE FOR A BASE POWER BATTERY INSTALL

RECOMMENDED CONFIGURATION

DOUBLE · 2 x 25 kWh UNITS (200A SERVICE + 9'-0" MIN. CLEAR WALL, BOTH PROVIDED)

NOTES:

1. THIS SCHEDULE SUMMARIZES INFORMATION SHOWN IN DETAIL ON SHEETS A1.0, E1.0 AND A3.0. WHERE A CONFLICT EXISTS, THE DETAIL SHEET GOVERNS.
2. AS-BUILT CONDITIONS SHALL BE FIELD VERIFIED BY THE INSTALLER PRIOR TO EQUIPMENT SET.
3. THIS IS AN ILLUSTRATIVE SAMPLE PREPARED FOR DEMONSTRATION; NOT A PERMITTED CONSTRUCTION DOCUMENT.

ARCHITECTURAL DRAWINGS

PROJECT
SINGLE-FAMILY RESIDENCE

RENOVATION · SERVICE UPGRADE

ADDRESS
8014 CHATEAU ST

HOUSTON, TX 77028

COUNTY
HARRIS · HCAD 0300170170004

USE / YEAR
A1 SINGLE-FAMILY · BUILT 1940

UTILITY
CENTERPOINT ENERGY

SERVICE
(N) 200A · 120/240V · OVERHEAD

SET
ARCH · A1.0 / E1.0 / A3.0 / A4.0

SCALE
NTS

SHEET NAME
BATTERY INSTALL COMPLIANCE SUMMARY

A4.0

ILLUSTRATIVE SAMPLE
NOT FOR CONSTRUCTION